



15, Jenkins Hse, Henry Rd,
Colaba, Mumbai, 400001.

MAKER TOWER

City/ State: MUMBAI, MAHARASHTRA

Client : MR. ASHOK HIREMATH

PLOT AREA: 0.00 Sq.Mt
BUILT-UP AREA: 0.00 Sq.Mt
TOTAL CARPET: 242.97 Sq.Mt
OR 2615.35 Sq.Ft

- NOTES:
- ALL DIMENSIONS ARE IN MM UNLESS SPECIFIED.
 - ALL DIMENOSN REFER TO FINISHED SURFACES.
 - ANY DETAIL OR DRAWING WILL NOT BE USED FOR CONSTRUCTION APART FROM THIS PROJECT.
 - ALL DRAWINGS SHOULD BE CHECKED & DIMENSIONS VERIFIED BY THE CONTRACTOR AND ANY AMBIGUITY BE BROUGHT TO THE NOTICE OF THE ARCHITECT BEFORE COMMENCEMENT OF SUCH WORK.
 - ALL STRUCTURAL DRAWINGS SHOULD BE READ SIMULTANEOUSLY WITH THE ARCHITECTURAL DRAWINGS.
 - NO MODIFICATIONS OR DEVIATIONS FROM ARCHITECTURAL DRAWINGS BE MADE WITHOUT PRIOR CONSULTATION WITH THE ARCHITECT.
 - ONLY WRITTEN DIMENSIONS SHOULD BE FOLLOWED.
 - FOR REINFORCEMENT DETAILS USE ONLY RCC DETAIL DRAWING.
 - ONLY THOSE DRAWINGS MARKED FOR EXECUTION WILL BE USED FOR CONSTRUCTION.
 - ANY DISCREPANCY IN THE DRAWING SHALL BE REPORTED TO THE CONSULTANT IMMEDIATELY.

- SPECIAL NOTES:
- AC & OUTDOOR UNIT LOCATION ARE INDICATIVE ONLY. REFER HVAC CONSULTANT DRAWINGS FOR DETAILS & ACCURATE LOCATIONS & ROUTING OF THE SAME.
 - FOR INTERNAL NICHE & FEATURES CHECK INTERIOR DRAWINGS.
 - FOR SLEEVES & PLUMBING CHECK MEP DRGS.
 - FOR OUTDOOR SERVICES POSITION & DETAILS REFER MEP DRAWINGS.
 - FOR LANDSCAPE PATTERN & DETAILS REFER LANDSCAPE DRAWINGS.

NO.	ISSUE	DATE

REVISION :

KEY PLAN

Date:
05.03.2025

Scale:
1:55 @A2

Project No:
A-X-xx-xx

Drawn By:
SN/ ST

STAMP & SIGN



ADVANCE COPY

GOOD FOR CONSTRUCTION

FLOOR PLAN

DRAWING NO.:

A-

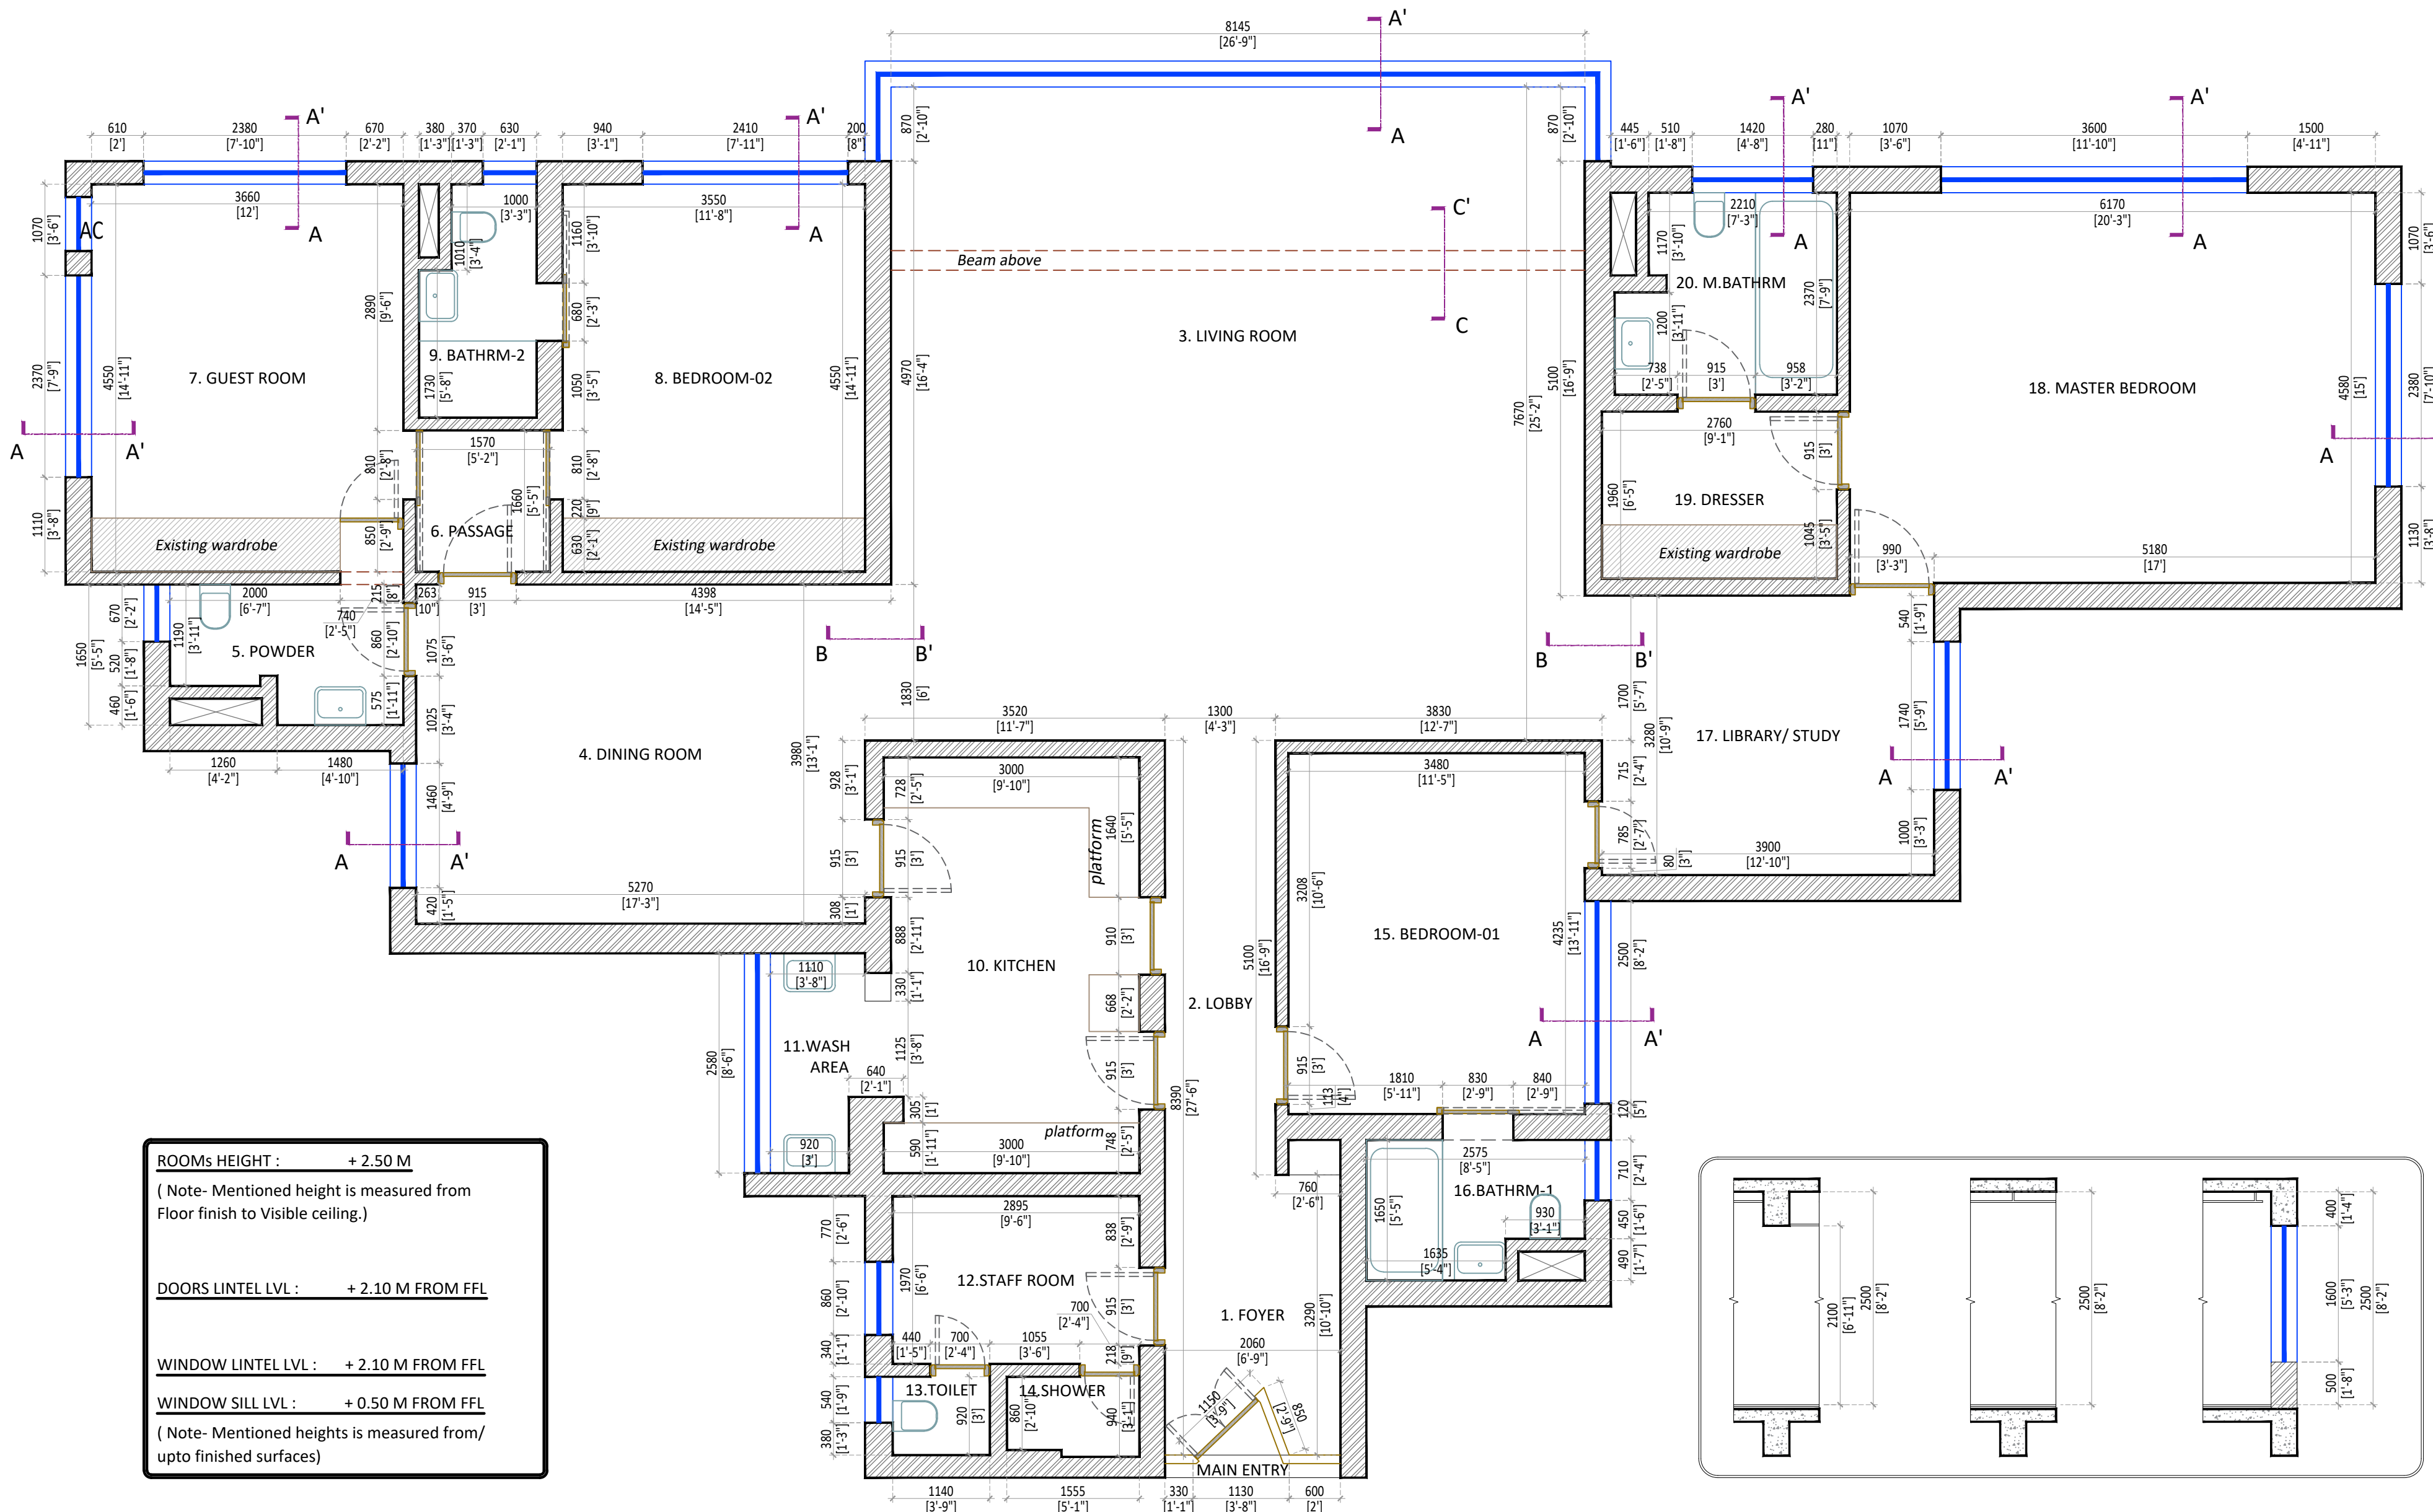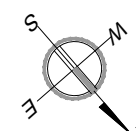

ROOMS HEIGHT : + 2.50 M
(Note- Mentioned height is measured from Floor finish to Visible ceiling.)

DOORS LINTEL LVL : + 2.10 M FROM FFL

WINDOW LINTEL LVL : + 2.10 M FROM FFL

WINDOW SILL LVL : + 0.50 M FROM FFL
(Note- Mentioned heights is measured from/ upto finished surfaces)

04 SECTION CC'
Scale 1:55

03 SECTION BB'
Scale 1:55

02 SECTION AA'-
Scale 1:55

01 FLOOR PLAN
Scale 1:55